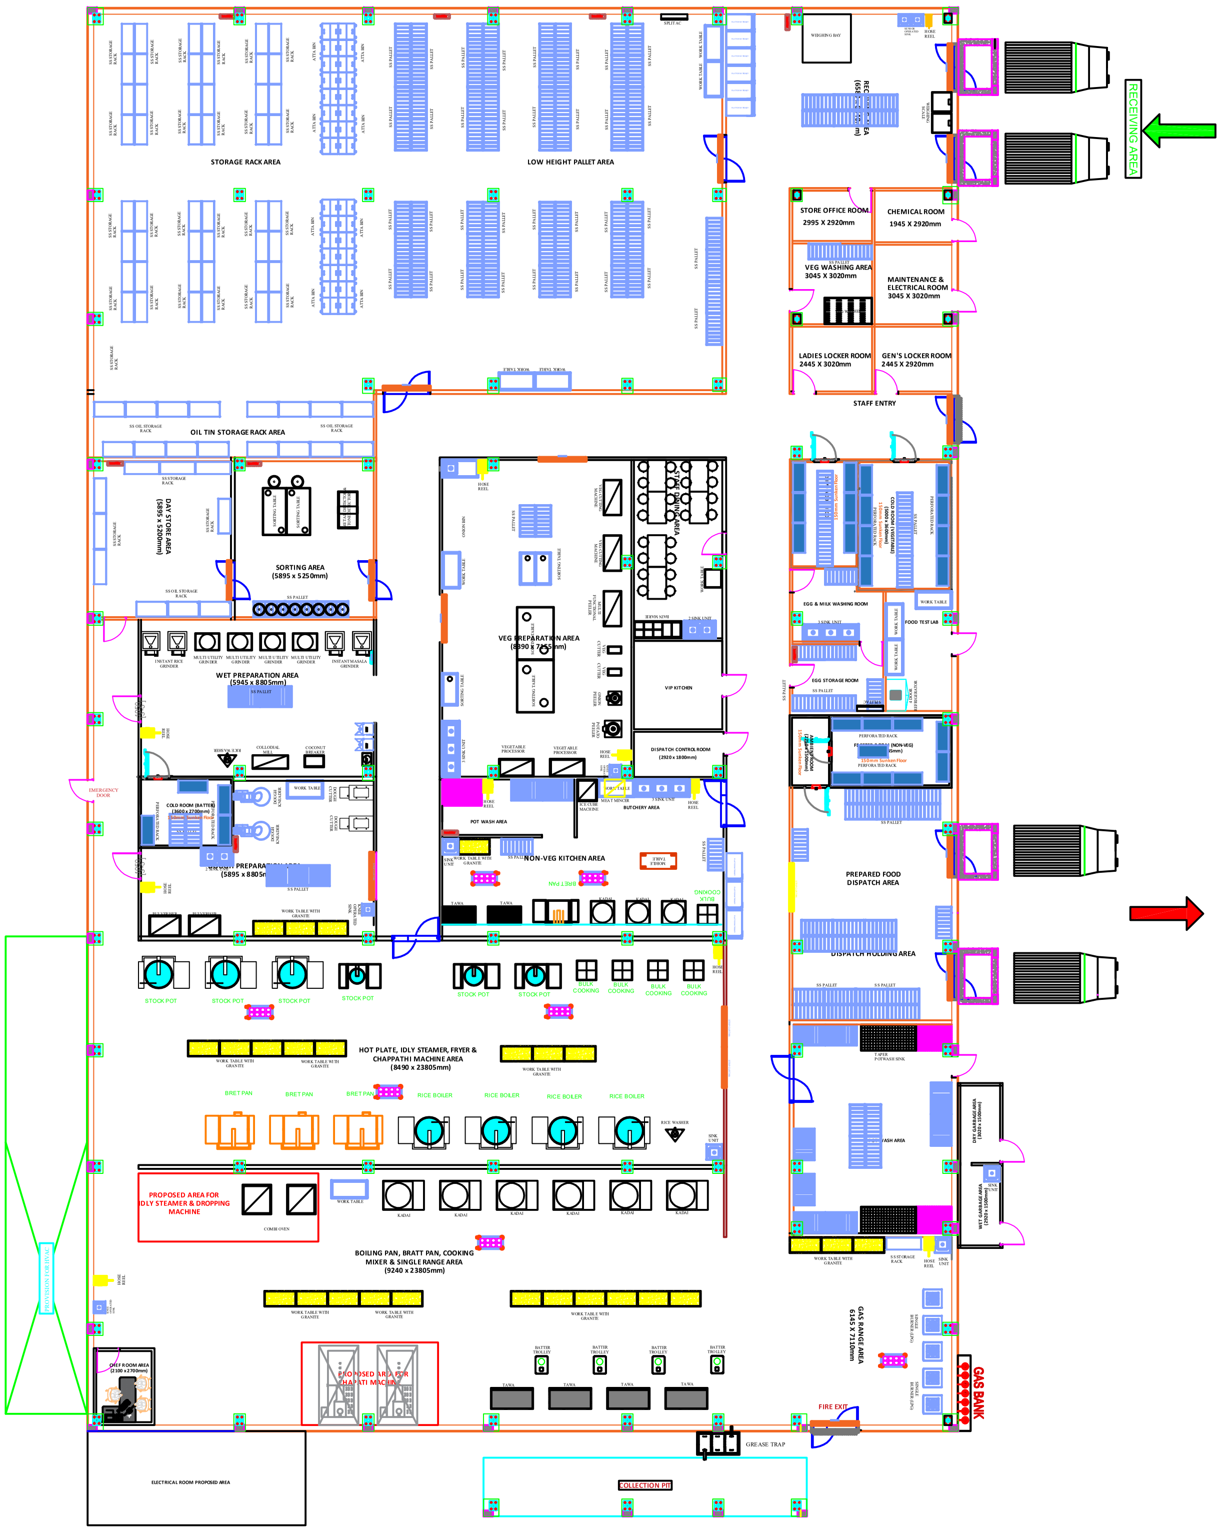
STORAGE RACK AREA
LOW HEIGHT PALLET AREA
SS STORAGE RACK
ATTA BIN
SS PALLET
WORK TABLE
SPLIT AC
WEIGHING BAY
RECEIVING AREA
STORE OFFICE ROOM
2995 X 2920mm
CHEMICAL ROOM
1945 X 2920mm
VEG WASHING AREA
3045 X 3020mm
MAINTENANCE & ELECTRICAL ROOM
3045 X 3020mm
LADIES LOCKER ROOM
2445 X 3020mm
GEN'S LOCKER ROOM
2445 X 2920mm
STAFF ENTRY
OIL TIN STORAGE RACK AREA
SS OIL STORAGE RACK
DAY STORE AREA
(5895 x 5200mm)
SORTING AREA
(5895 x 5250mm)
SORTING TABLE
STAFF DINING AREA
VEG PREPARATION AREA
(8390 x 7765mm)
VEGETABLE PROCESSOR
VIP KITCHEN
DISPATCH CONTROL ROOM
(2920 x 1800mm)
WET PREPARATION AREA
(5945 x 8805mm)
INSTANT RICE GRINDER
MULTI UTILITY GRINDER
INSTANT MASALA GRINDER
COLLOIDAL MILL
COCONUT BREAKER
EMERGENCY DOOR
COLD ROOM (BATTER)
(3600 x 2700mm)
PERFORATED RACK
DOUGH KNEADER
PREPARATION AREA
(5895 x 8805mm)
WORK TABLE WITH GRANITE
POT WASH AREA
BUTCHERY AREA
MEAT MINCER
ICE CUBE MACHINE
3 SINK UNIT
NON-VEG KITCHEN AREA
BRETT PAN
BULK COOKING
TAWA
KADAI
EGG & MILK WASHING ROOM
FOOD TEST LAB
EGG STORAGE ROOM
COLD ROOM (VEGETABLE)
(5000 x 3600mm)
150mm Sunken Floor
COLD ROOM (NON-VEG)
PREPARED FOOD DISPATCH AREA
DISPATCH HOLDING AREA
STOCK POT
HOT PLATE, IDLY STEAMER, FRYER & CHAPPATHI MACHINE AREA
(8490 x 23805mm)
BRET PAN
RICE BOILER
RICE WASHER
HOSE REEL
SINK UNIT
PROPOSED AREA FOR IDLY STEAMER & DROPPING MACHINE
COMBI OVEN
BOILING PAN, BRATT PAN, COOKING MIXER & SINGLE RANGE AREA
(9240 x 23805mm)
WASH AREA
3 SINK POTWASH SINK
DRY GARBAGE AREA
(3020 x 1500mm)
WET GARBAGE AREA
(2920 x 1500mm)
GAS RANGE AREA
6145 X 7110mm
SINGLE BURNER (GAS)
GAS BANK
FIRE EXIT
BATTER TROLLEY
PROVISION FOR HVAC
DG ROOM AREA
(3100 x 2700mm)
PROPOSED AREA FOR CHAPATI MACHINE
GREASE TRAP
COLLECTION PIT
ELECTRICAL ROOM PROPOSED AREA